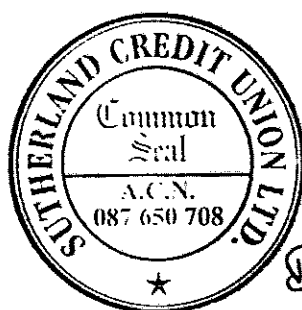


SIGNATURE AND SEALS ONLY.

Paul Brooks
PAUL BROOKS

K. THOMAS

K. THOMAS

N.J. THOMAS

THE LOCATION OF MEAN HIGH WATER MARK HAS BEEN APPROVED BY THE GENERAL MANAGER, LAND N.S.W. DEPT. OF LAND AND WATER CONSERVATION IN FILE MNOI H77.

Crown Lands Office Approval

PLAN APPROVED
Authorised Officer
Land District
Paper No.
Field Book pages

Subdivision Certificate

I certify that the provisions of s.109J of the Environmental Planning and Assessment Act 1979 have been satisfied in relation to the proposed subdivision.

Subdivision set out herein

Consent authority: The Council of Sutherland Shire

Date of endorsement: 12/3/01

Accreditation No.: 69/2001

Subdivision Certificate No.: 69/2001


File No.: PR/2325

Note: When the plan is to be lodged electronically in the Land Titles Office, it should include a signature in an electronic or digital format approved by the Registrar-General.

Delete whichever is inapplicable

SURVEYOR'S REFERENCE: 19830 P.F./BUNARBA

(CHECKLIST)

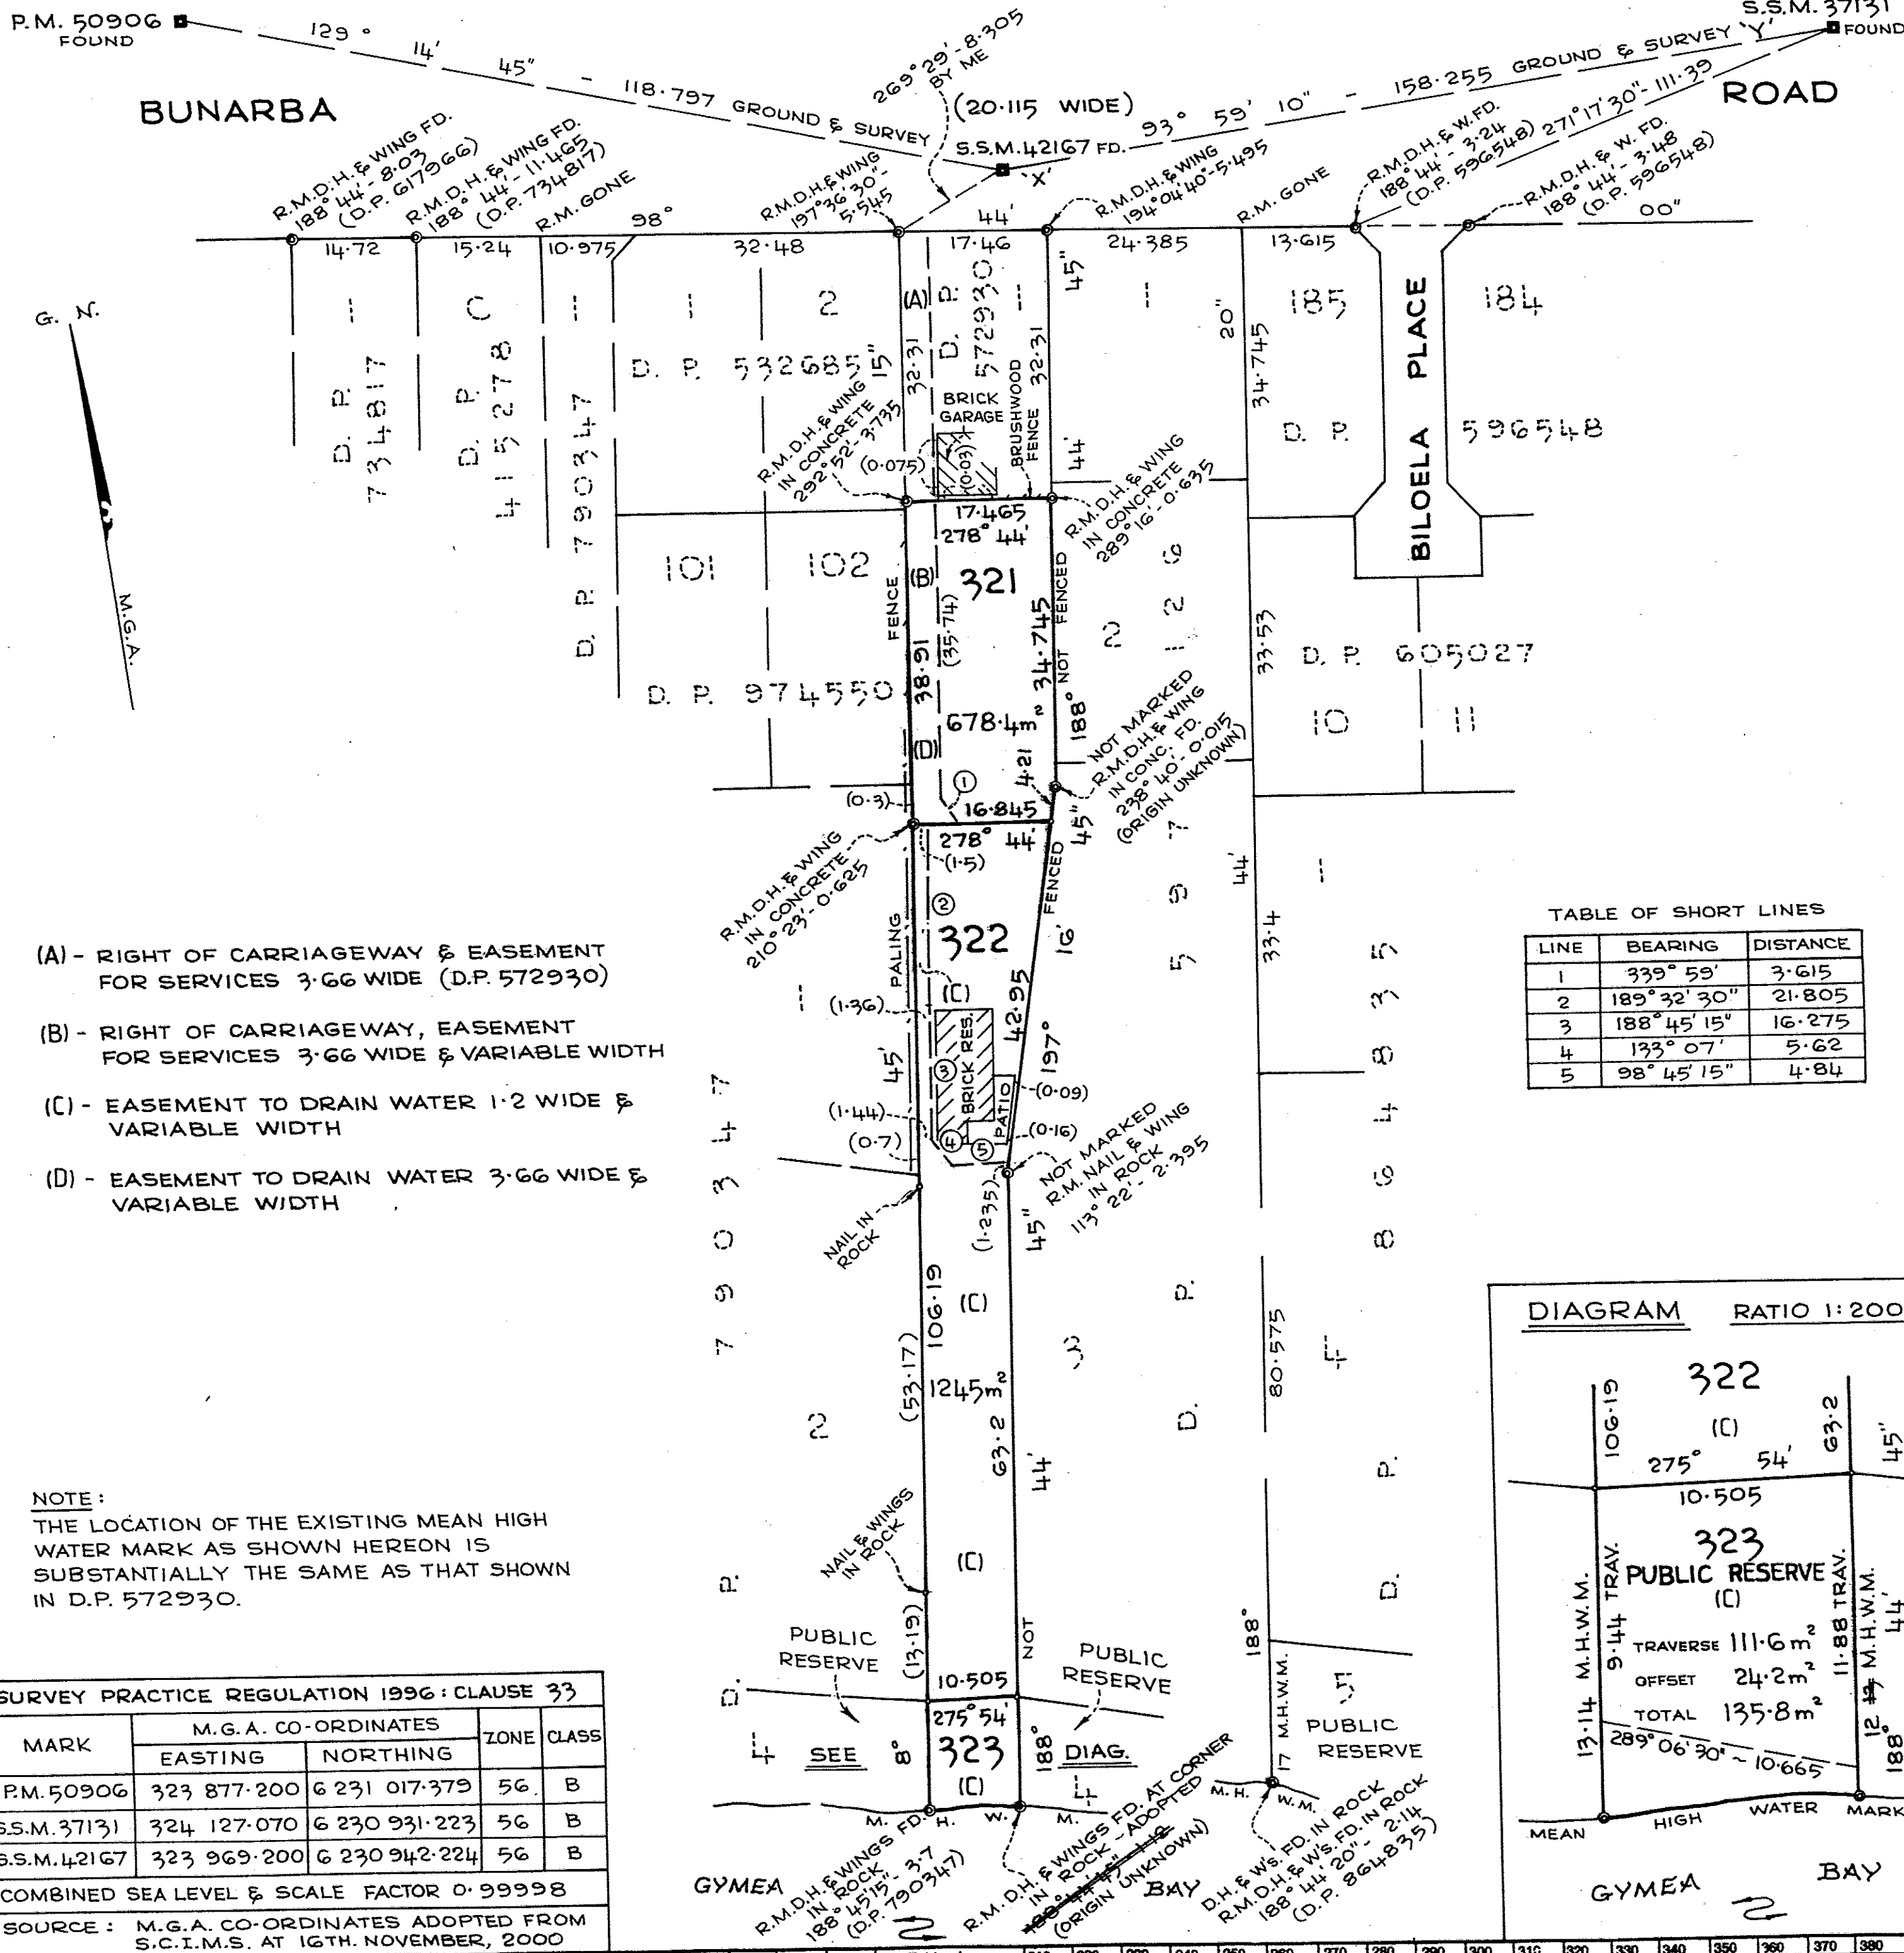

DP1025901

Registered: 11/3-5-2001

C.A: SEE CERTIFICATE

Title System: TORRENS

Purpose: SUBDIVISION

Ref. Map: U0030-94#

Last Plan: DP572930

PLAN OF SUBDIVISION OF
LOT 2 IN D.P. 572930

Lengths are in metres. Reduction Ratio 1: 600

LGA SUTHERLAND SHIRE

Locality: GYMEA BAY

Parish: SUTHERLAND

County: CUMBERLAND

This is sheet 1 of my plan in
(Delete if inapplicable) sheets.

Surveyors (Practice) Regulation 1996
PETER GABRIEL FRIEDMANN
HARRISON FRIEDMANN & ASSOC. PTY. LTD.
P.O. BOX 99 JANNALI N.S.W. 2226
a surveyor registered under the Surveyors Act, 1929, hereby certify
that the survey represented in this plan is accurate, has been made in
accordance with the Surveyors (Practice) Regulation 1996 and was
completed on 19TH FEBRUARY, 2001
The survey relates to LOTS 321, 322 & 323

(here specify the land actually surveyed or specify any land shown in
the plan that is not the subject of the survey)

Datum: X-Y
Zone: Suburban
(Signature) P.G. Friedman
Surveyor registered under
the Surveyors Act 1929

Plans used in preparation of survey/compilation:
D.P. 572930
D.P. 596548
D.P. 597126
D.P. 790347
D.P. 864835

PANEL FOR USE ONLY for statements of intention
to dedicate public roads, to create public reserves,
drainage reserves, easements, restrictions on the
use of land or positive covenants.

PURSUANT TO SEC.88B OF THE
CONVEYANCING ACT 1919 IT IS
INTENDED TO CREATE :-

1. RIGHT OF CARRIAGEWAY
3.66 WIDE & VARIABLE WIDTH
2. EASEMENT FOR SERVICES
3.66 WIDE & VARIABLE WIDTH
3. EASEMENT TO DRAIN WATER
1.2 WIDE & VARIABLE WIDTH
4. EASEMENT TO DRAIN WATER
3.66 WIDE & VARIABLE WIDTH
5. RESTRICTION ON THE USE
OF LAND.
6. POSITIVE COVENANT
7. POSITIVE COVENANT

IT IS INTENDED TO DEDICATE
LOT 323 TO THE PUBLIC AS
PUBLIC RESERVE.

DISTANCE 12 TO M.H.W.M. TRAVERSE CONNECTION 289° 06' 30" ~ 10.665 ADDED & CONNECTION 188° 44' 45" ~ 112 STRUCK THROUGH AND
AT CORNER - ADOPTED ADDED AT SURVEYORS REQUEST